

PLOT DETAILS

Plot Number

3261208

Plot Area

2,117.05 m²
22,787.74 ft²

Maximum GFA

15,285.95 m²
164,536.60 ft²

Maximum Coverage

N/A

Maximum Height

G+14

Setbacks (m)

Side	Building	Podium
1	SEE NOTES	SEE NOTES
2	SEE NOTES	SEE NOTES
3	SEE NOTES	SEE NOTES
4	SEE NOTES	SEE NOTES

Land Use

- **COMMERCIAL:** OFFICES, RETAIL
- **HOSPITALITY:** HOTEL
- **RESIDENTIAL:** APARTMENT

Master Developer


Project Name

SAMA AL JADAF

Community Name

Al Jadaf

Location Map

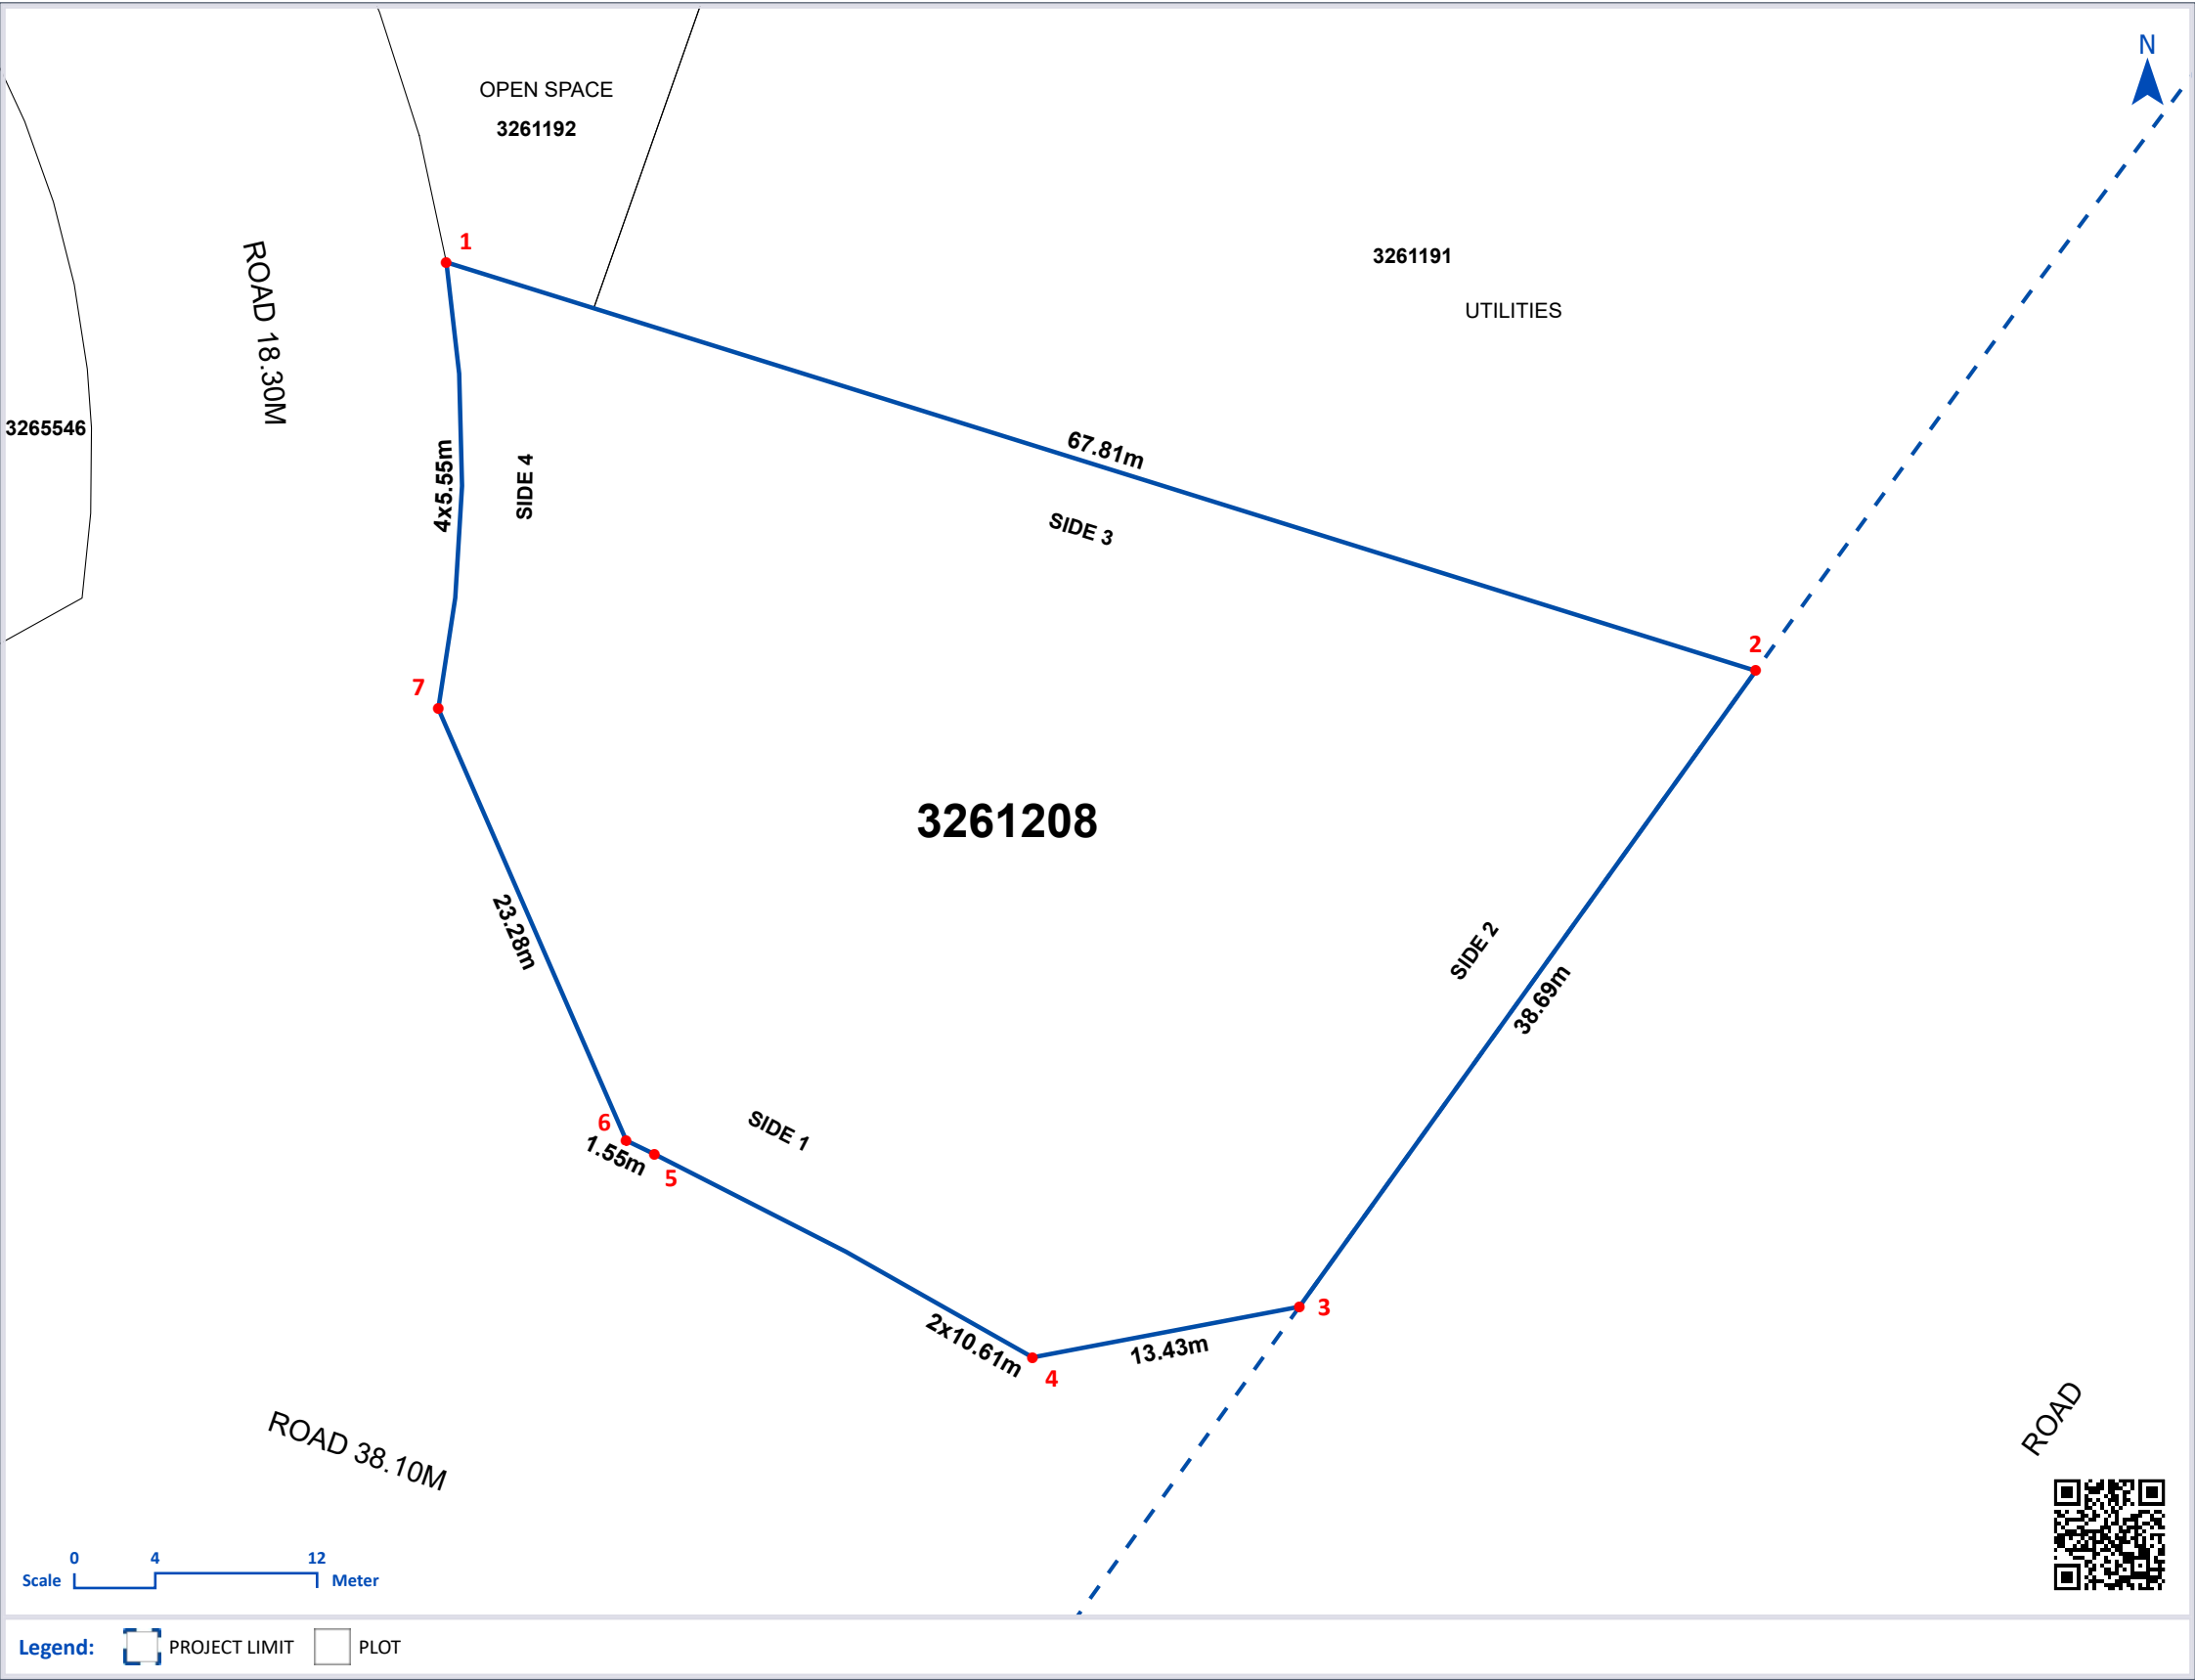

General Notes

- **PARKING:** FOR APARTMENT, ONE BAY FOR EACH UNIT LESS THAN OR EQUAL TO 150 SQ.M GFA AND TWO BAYS FOR EACH UNIT EXCEEDING 150 SQ.M GFA; FOR HOTEL, ONE BAY FOR EACH 5 HOTEL ROOMS AND ONE BAY FOR EACH 2 SUITES AND ONE BAY FOR EACH 50 SQ.M NET AREA OF FOOD AND BEVERAGE, MANAGEMENT OFFICE AND RETAIL AREAS AND ONE BAY FOR EACH 20 SQ.M NET AREA OF MEETING AND BALLROOM HALL AREA; FOR OFFICES, ONE BAY FOR EACH 50 SQ.M OF OFFICE NET AREA; FOR RETAIL, ONE BAY FOR EACH 70 SQ.M OF RETAIL NET AREA.
- **SETBACK:** FOR PODIUM NOT MANDATORY, FOR BUILDING QUARTER OF THE HEIGHT FROM NEIGHBORING PLOTS AND FROM CENTER OF SIKKA - MAXIMUM 7.5M AND A MINIMUM OF 3M.
- **NOC** FROM DUBAI MUNICIPALITY COASTAL ZONE AND WATERWAYS MANAGEMENT SECTION TO BE OBTAINED.
- **RETAIL** IS RESTRICTED ON THE GROUND FLOOR ONLY.
- THE DISTRIBUTION OF LAND USE AND RELEVANT GFA IS SUBJECT TO PLANNING, UTILITIES AND TRAFFIC APPROVED STUDIES.

Disclaimer: This document is for illustration purposes only. The final and authoritative data can be obtained through Site Plan and Demarcation Certificate requests.

For live information please scan the QR code or visit <https://gis.dda.gov.ae/dis/?PlotNumber=3261208>

Print Date: 03/05/2026 10:08 AM